


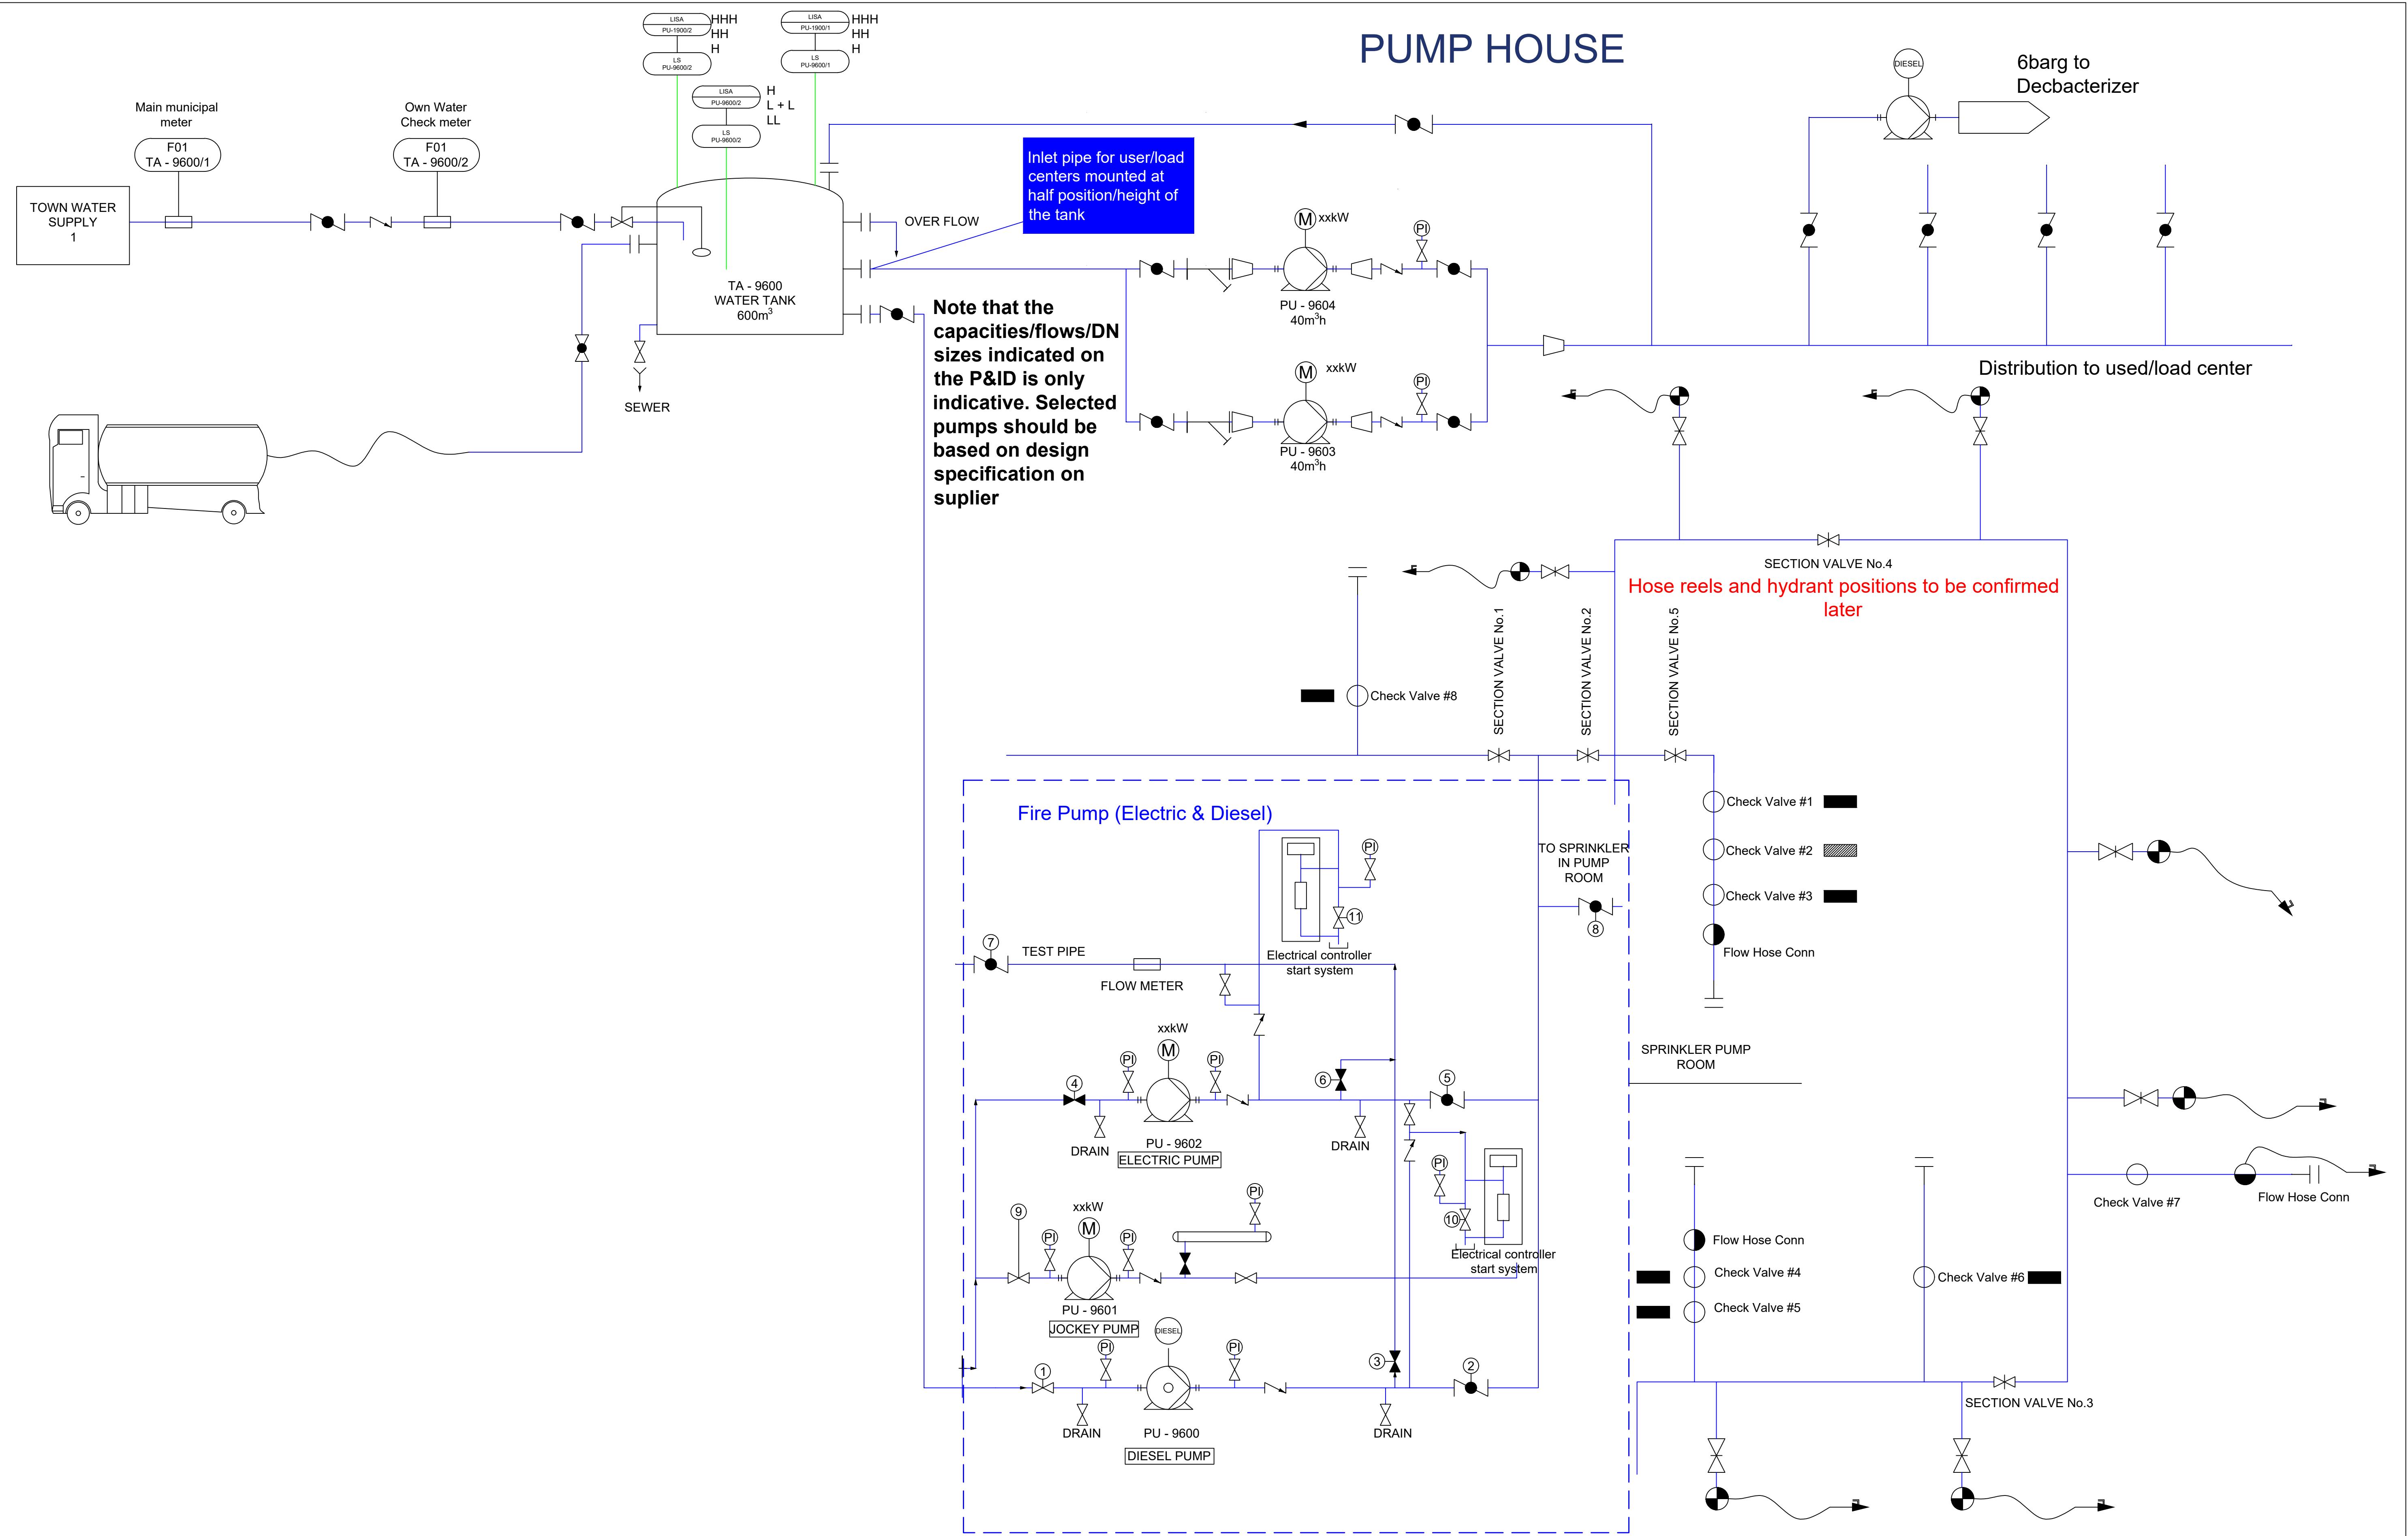

CLIENT		FCL PROCESSING		/Desktop/Picture1.jpg	
TITLE		PIPING & INSTRUMENTATION DIAGRAM TOWN WATER INTAKE, STROAGE, PUMP HOUSE & DISTRIBUTION SYSTEM			
DRAWN BY		GODWIN OCLOO			SIZE A0
SUPERVISED BY		RICHARDSON ADU-GYAMFI			
APPROVED BY		RICHARD NKRUMAH			
SCALE	CAD NO. XXXXXX-00-PID-0001	PROJECT NO. XXXXXX	DRAWING NO. XXXXXX-00-PID-0001-01		REF 001